Common Enclosure Section

IP65/ IP67 construction guidance | gasket, standoffs, cable glands, airflow path

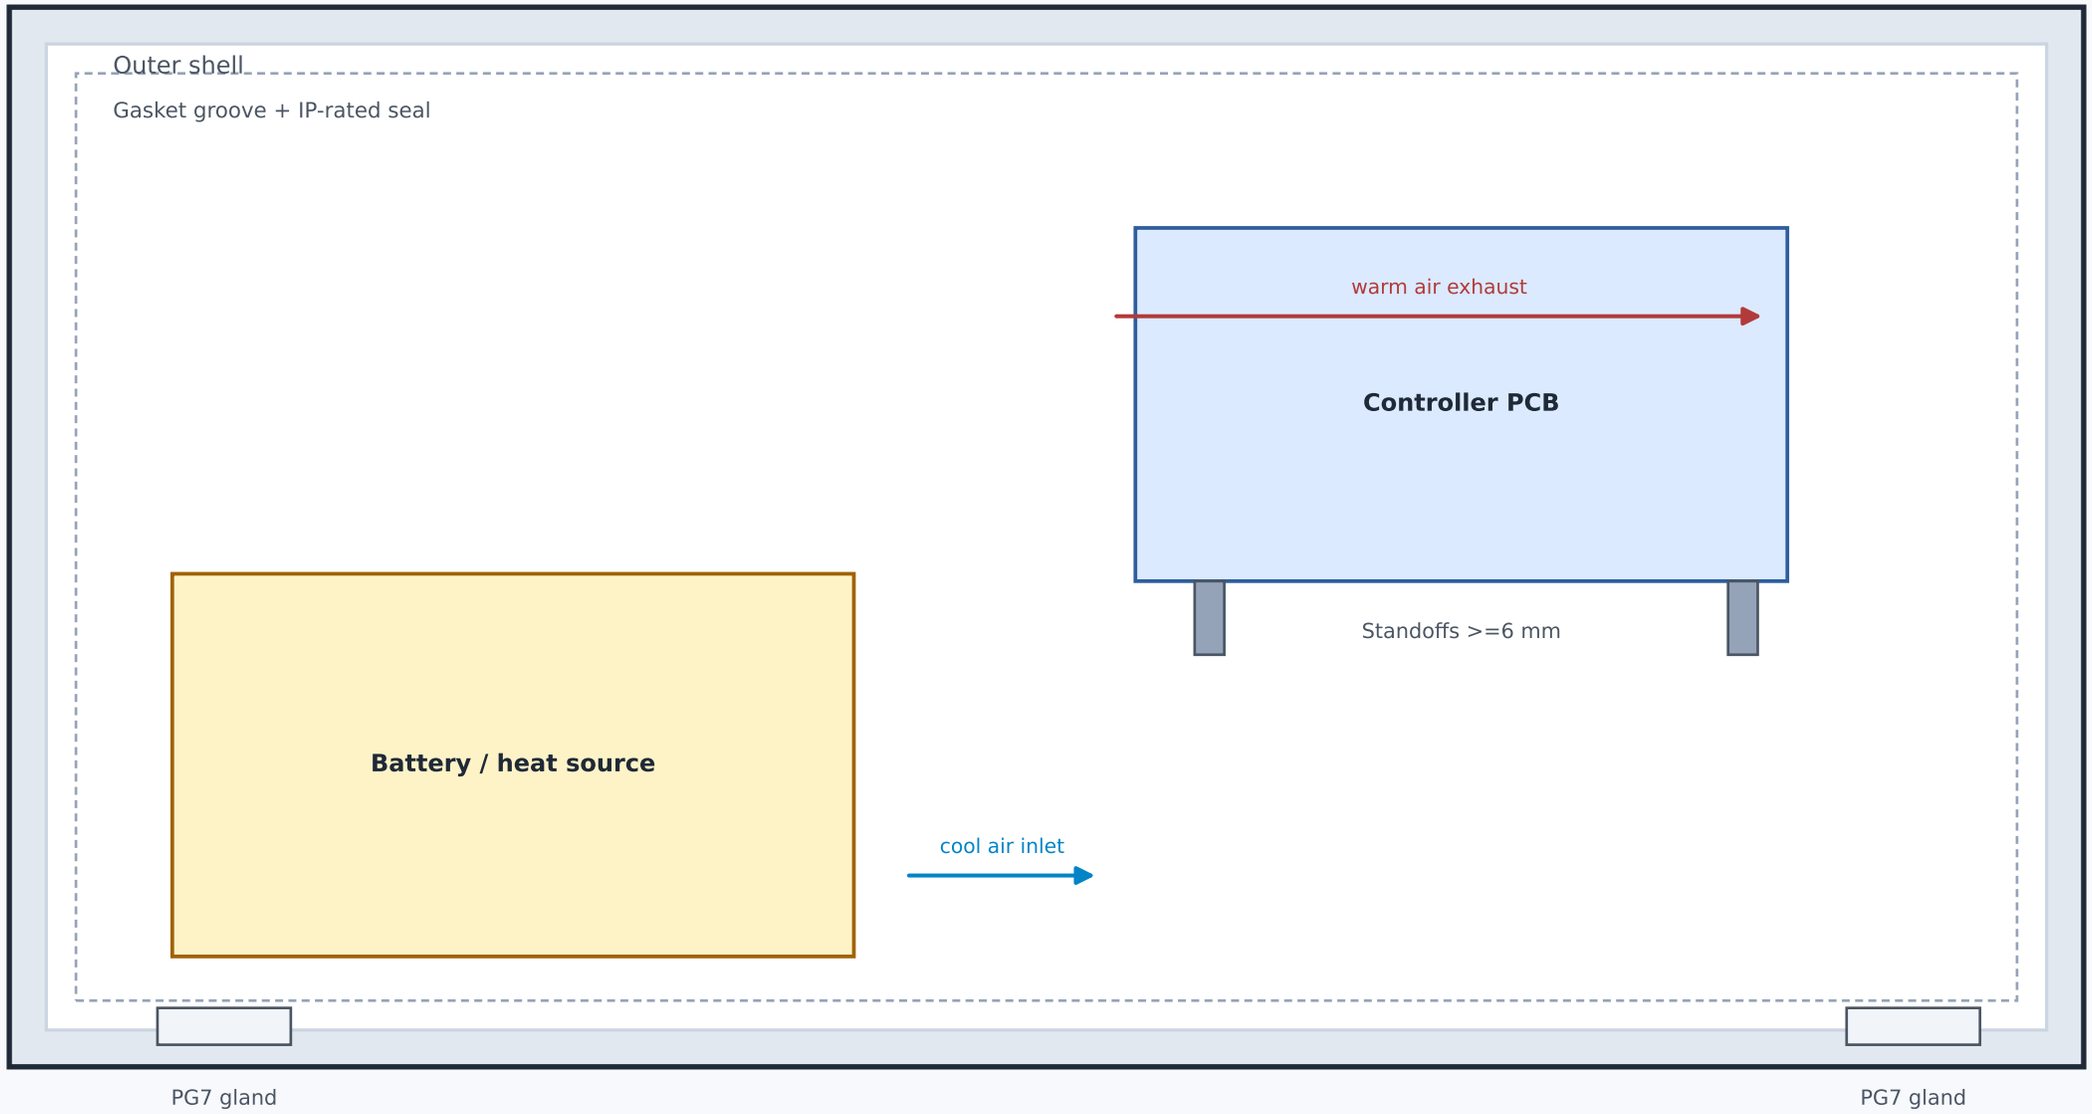

Rules: gasket compression 30-40%, desiccant, drip loop, service loop, separate HV/LV glands, conformal coating.

Generated by hardware/diagrams/generate_diagrams.py | final enclosure must pass IP and thermal validation